



LET'S WORK  
TOGETHER AND  
CREATE  
SOMETHING GREAT



LINKEDIN.COM/IN/IMANIHAUPT  
INSTAGRAM@ARQ.WELL

IMANIHAUPT.COM

720-660-7119

# ARCH-DESIGNER

## PLAN DESIGN SAMPLES

Imani Haupt, Thomas Cooke, Shane Inman


## THE BUILDING

### FLOOR PLANS



#### FLEX MARKET

The standard 15' column grid is partitioned with wall modules up to 12 additional increments up to 4800 SF of surface space, often community room market vendor space available space for kiosk parties

#### LEVEL 1

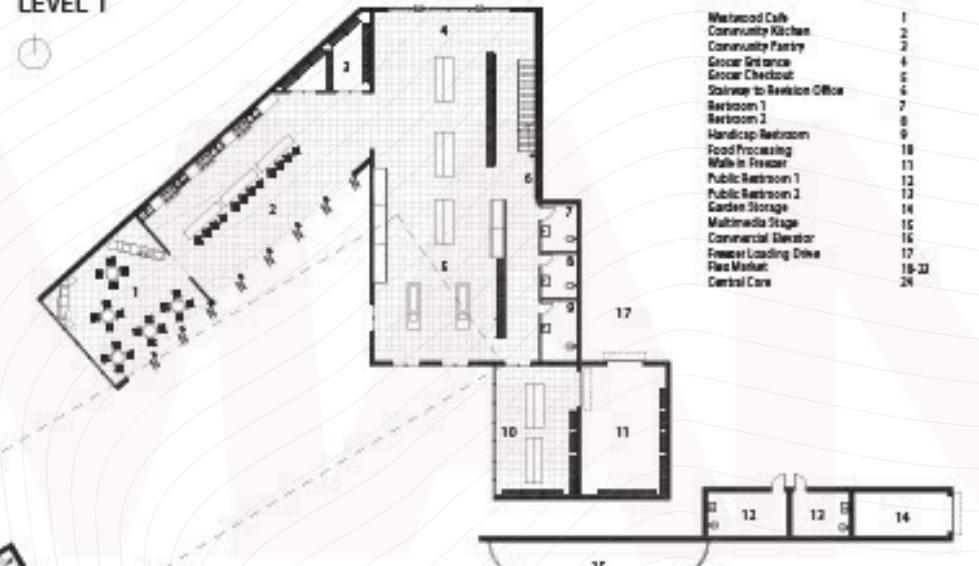






#### LEVEL 2

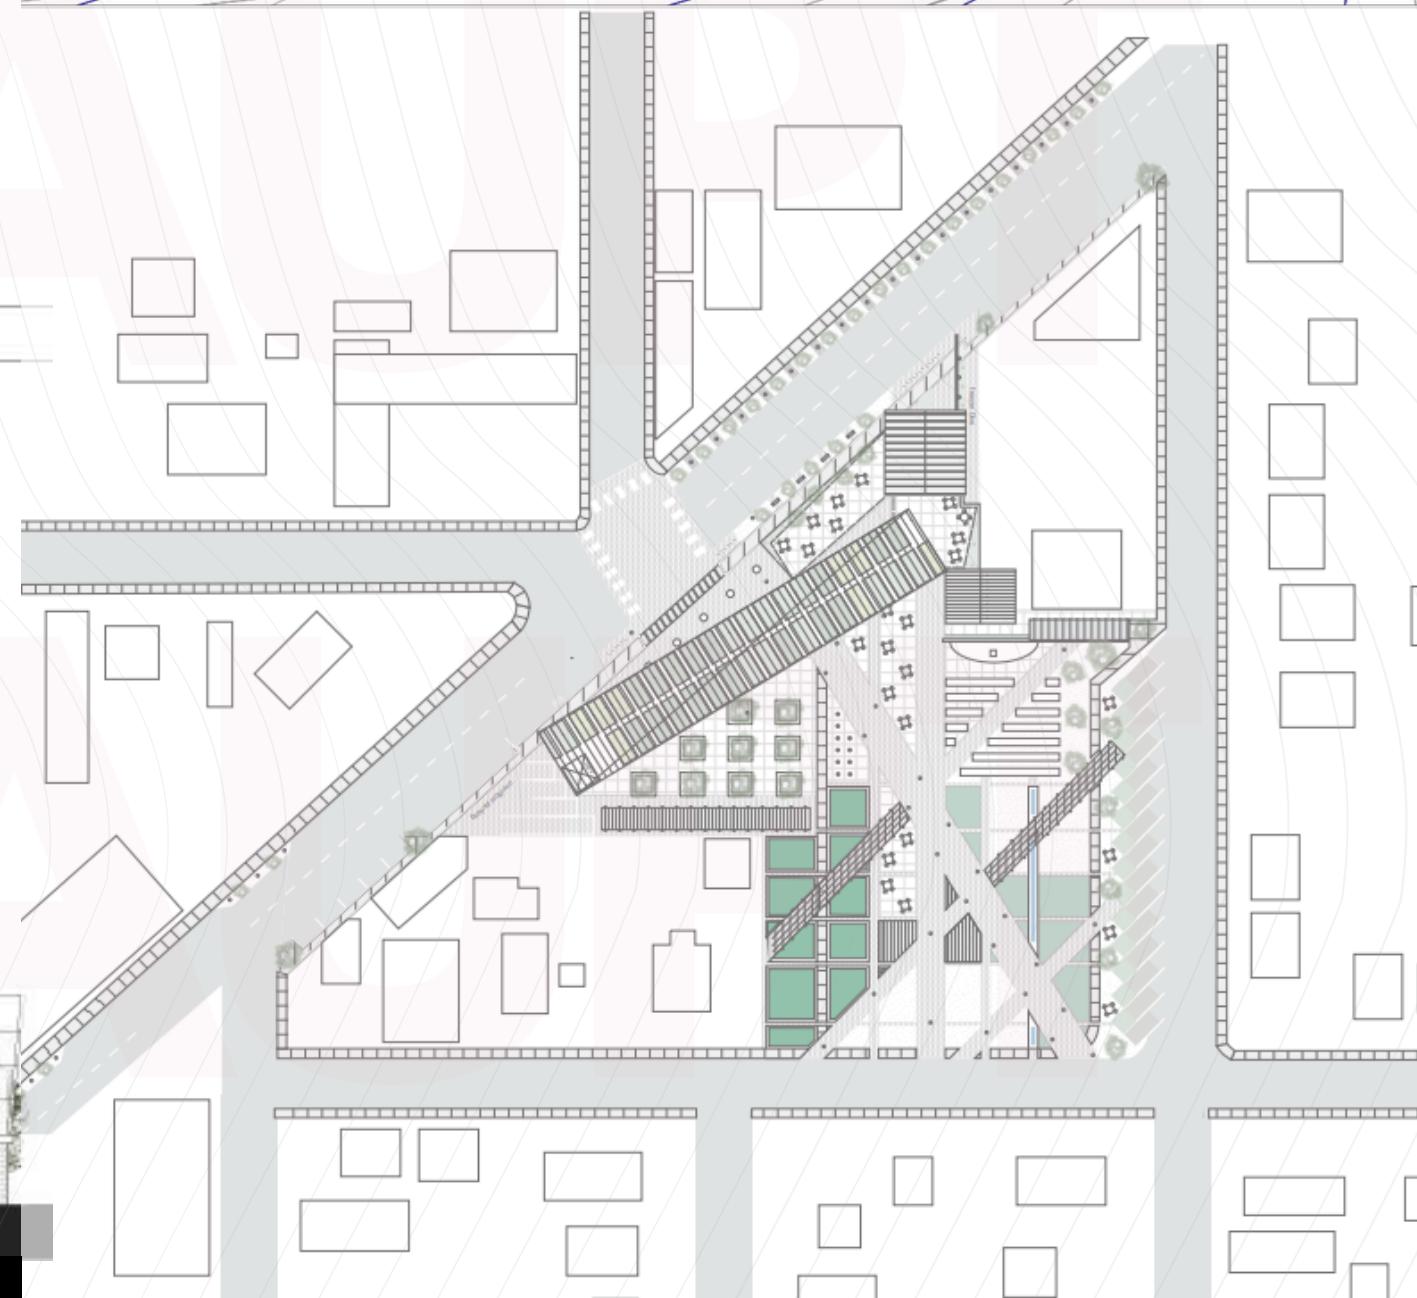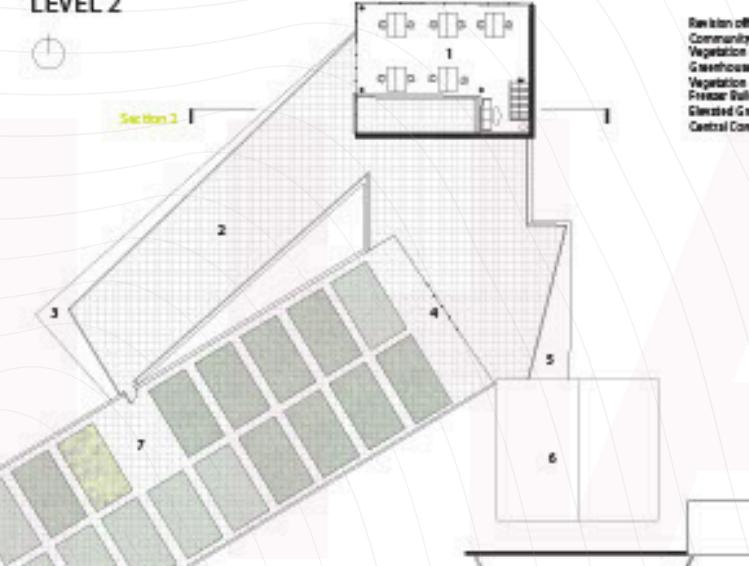

### SECTION 2

facing South



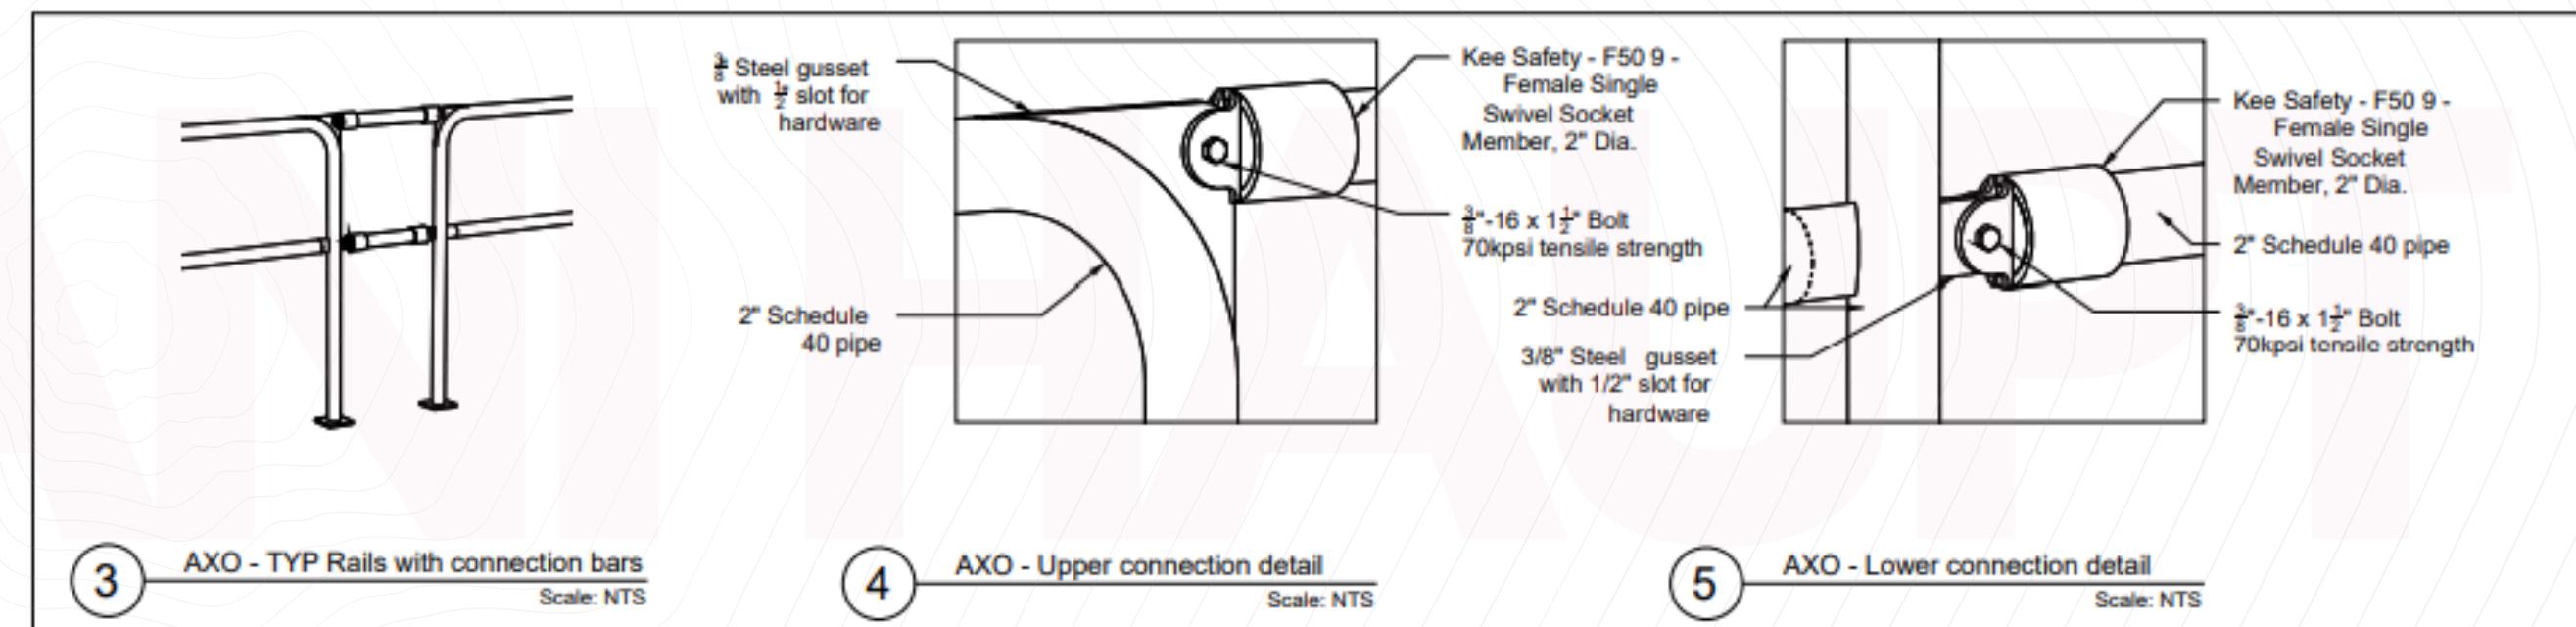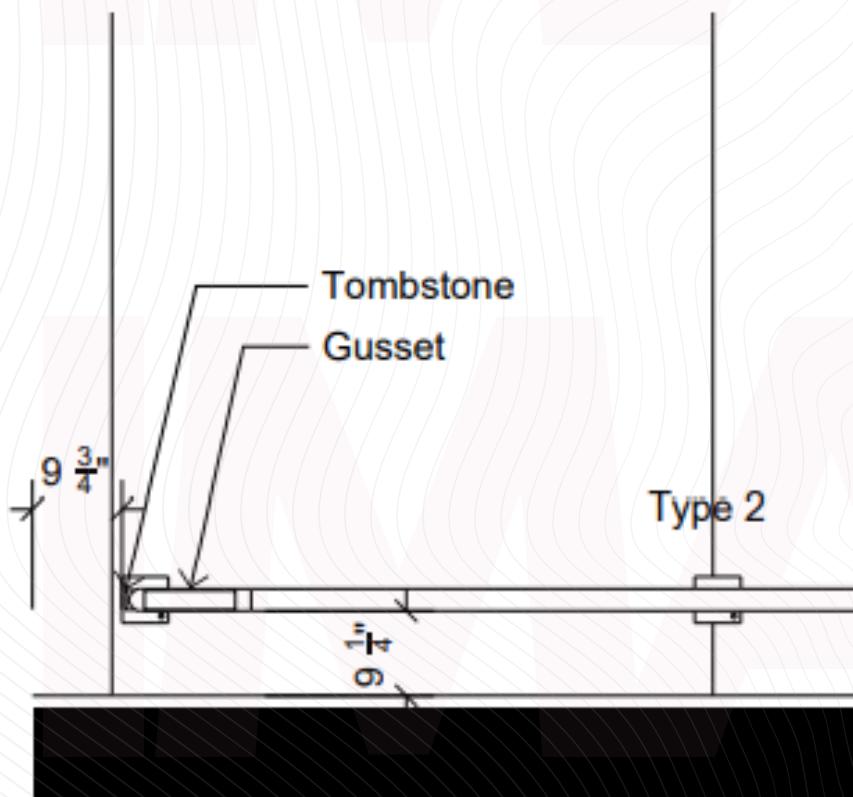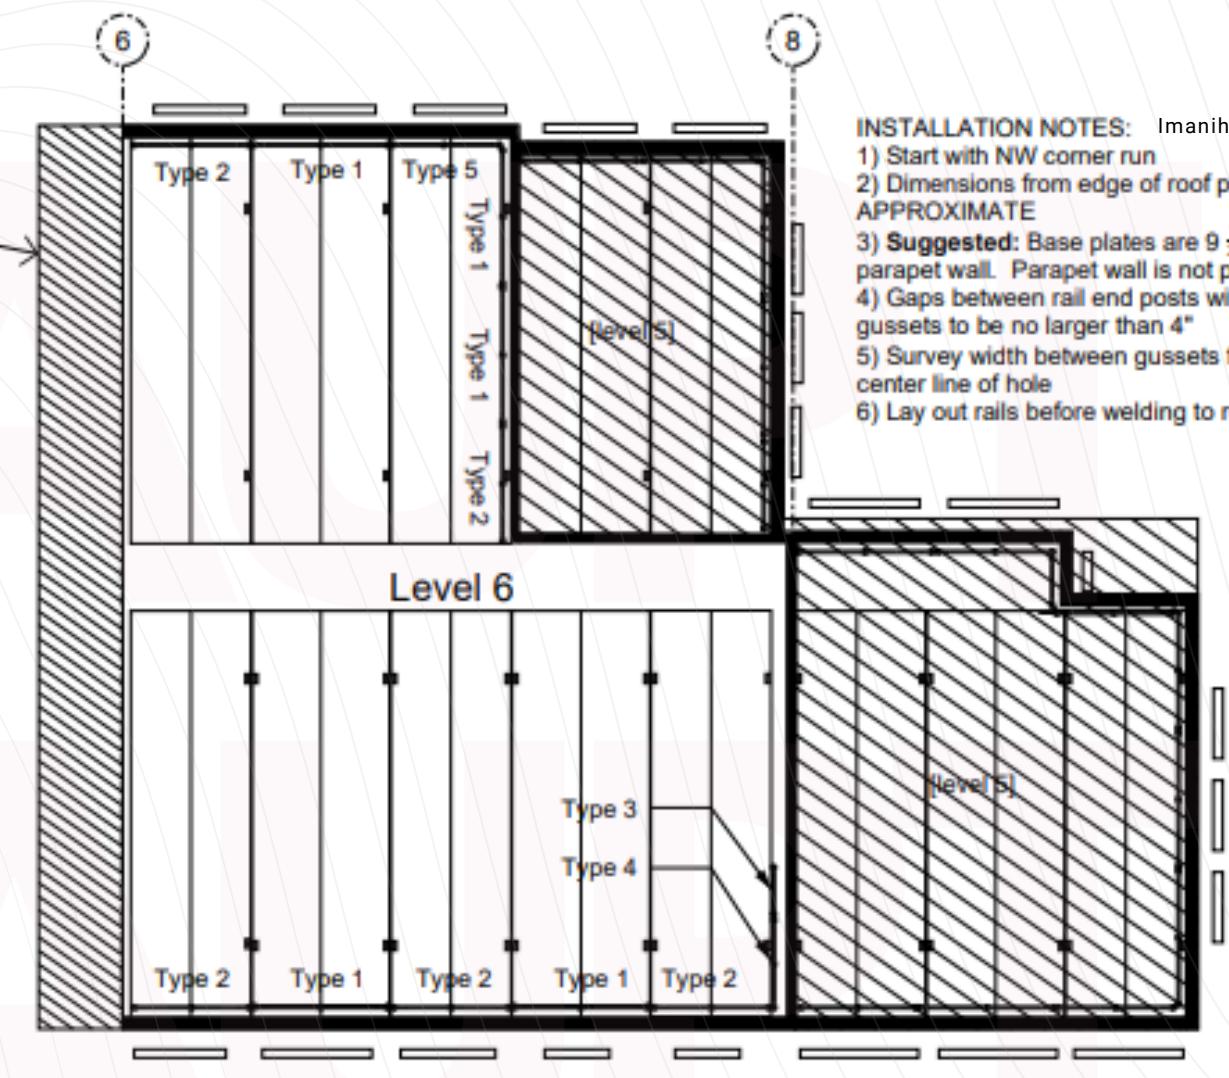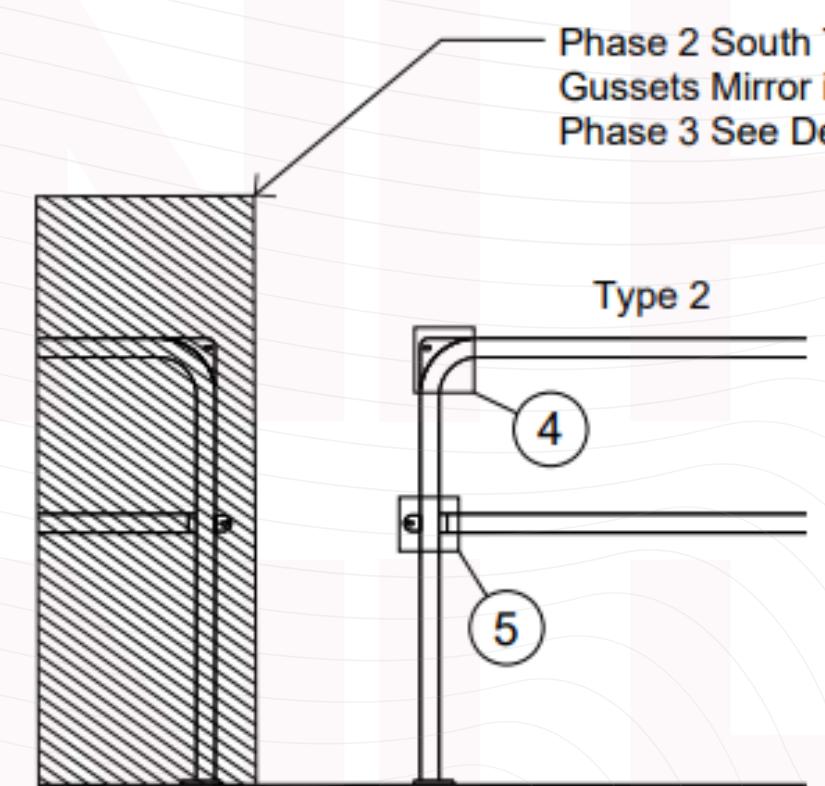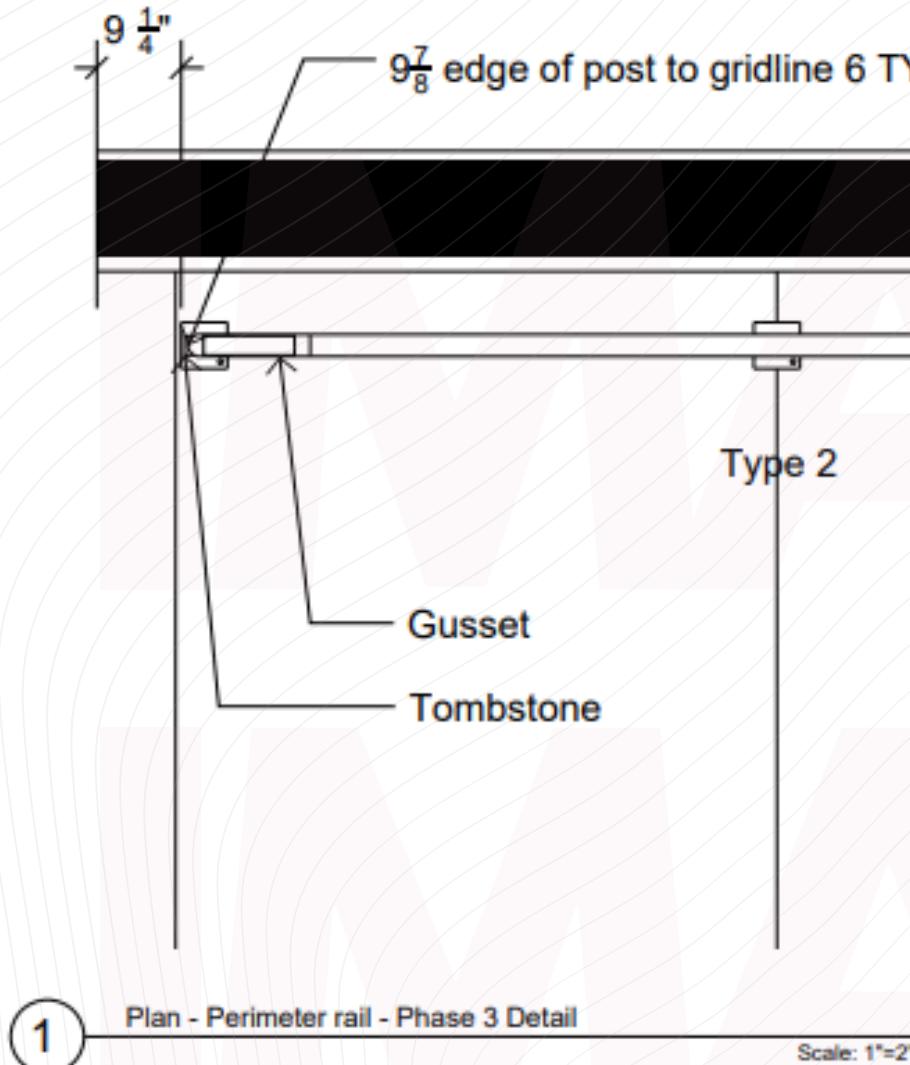


B From [Roof Top - Perimeter Rail - Connection Bar Details Sheet #0.02]

INSTALLATION NOTES: lmanihaft.com

- 1) Start with NW corner run
- 2) Dimensions from edge of roof plates APPROXIMATE
- 3) Suggested: Base plates are  $9\frac{1}{2} \pm$  off parapet wall. Parapet wall is not plane
- 4) Gaps between rail end posts without gussets to be no larger than 4"
- 5) Survey width between gussets from center line of hole
- 6) Lay out rails before welding to roof


# ARCH-DESIGNER

PLAN DESIGN SAMPLES

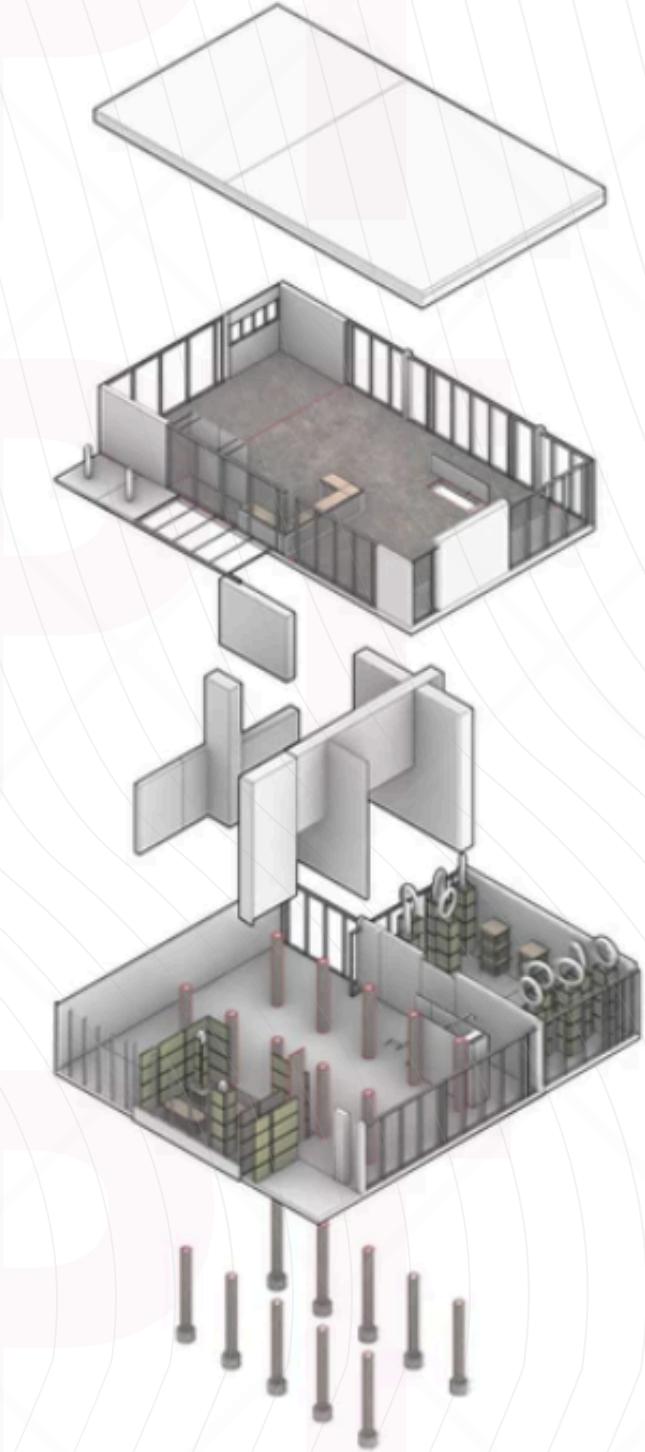


# ARCH-DESIGNER

## PLAN DESIGN SAMPLES

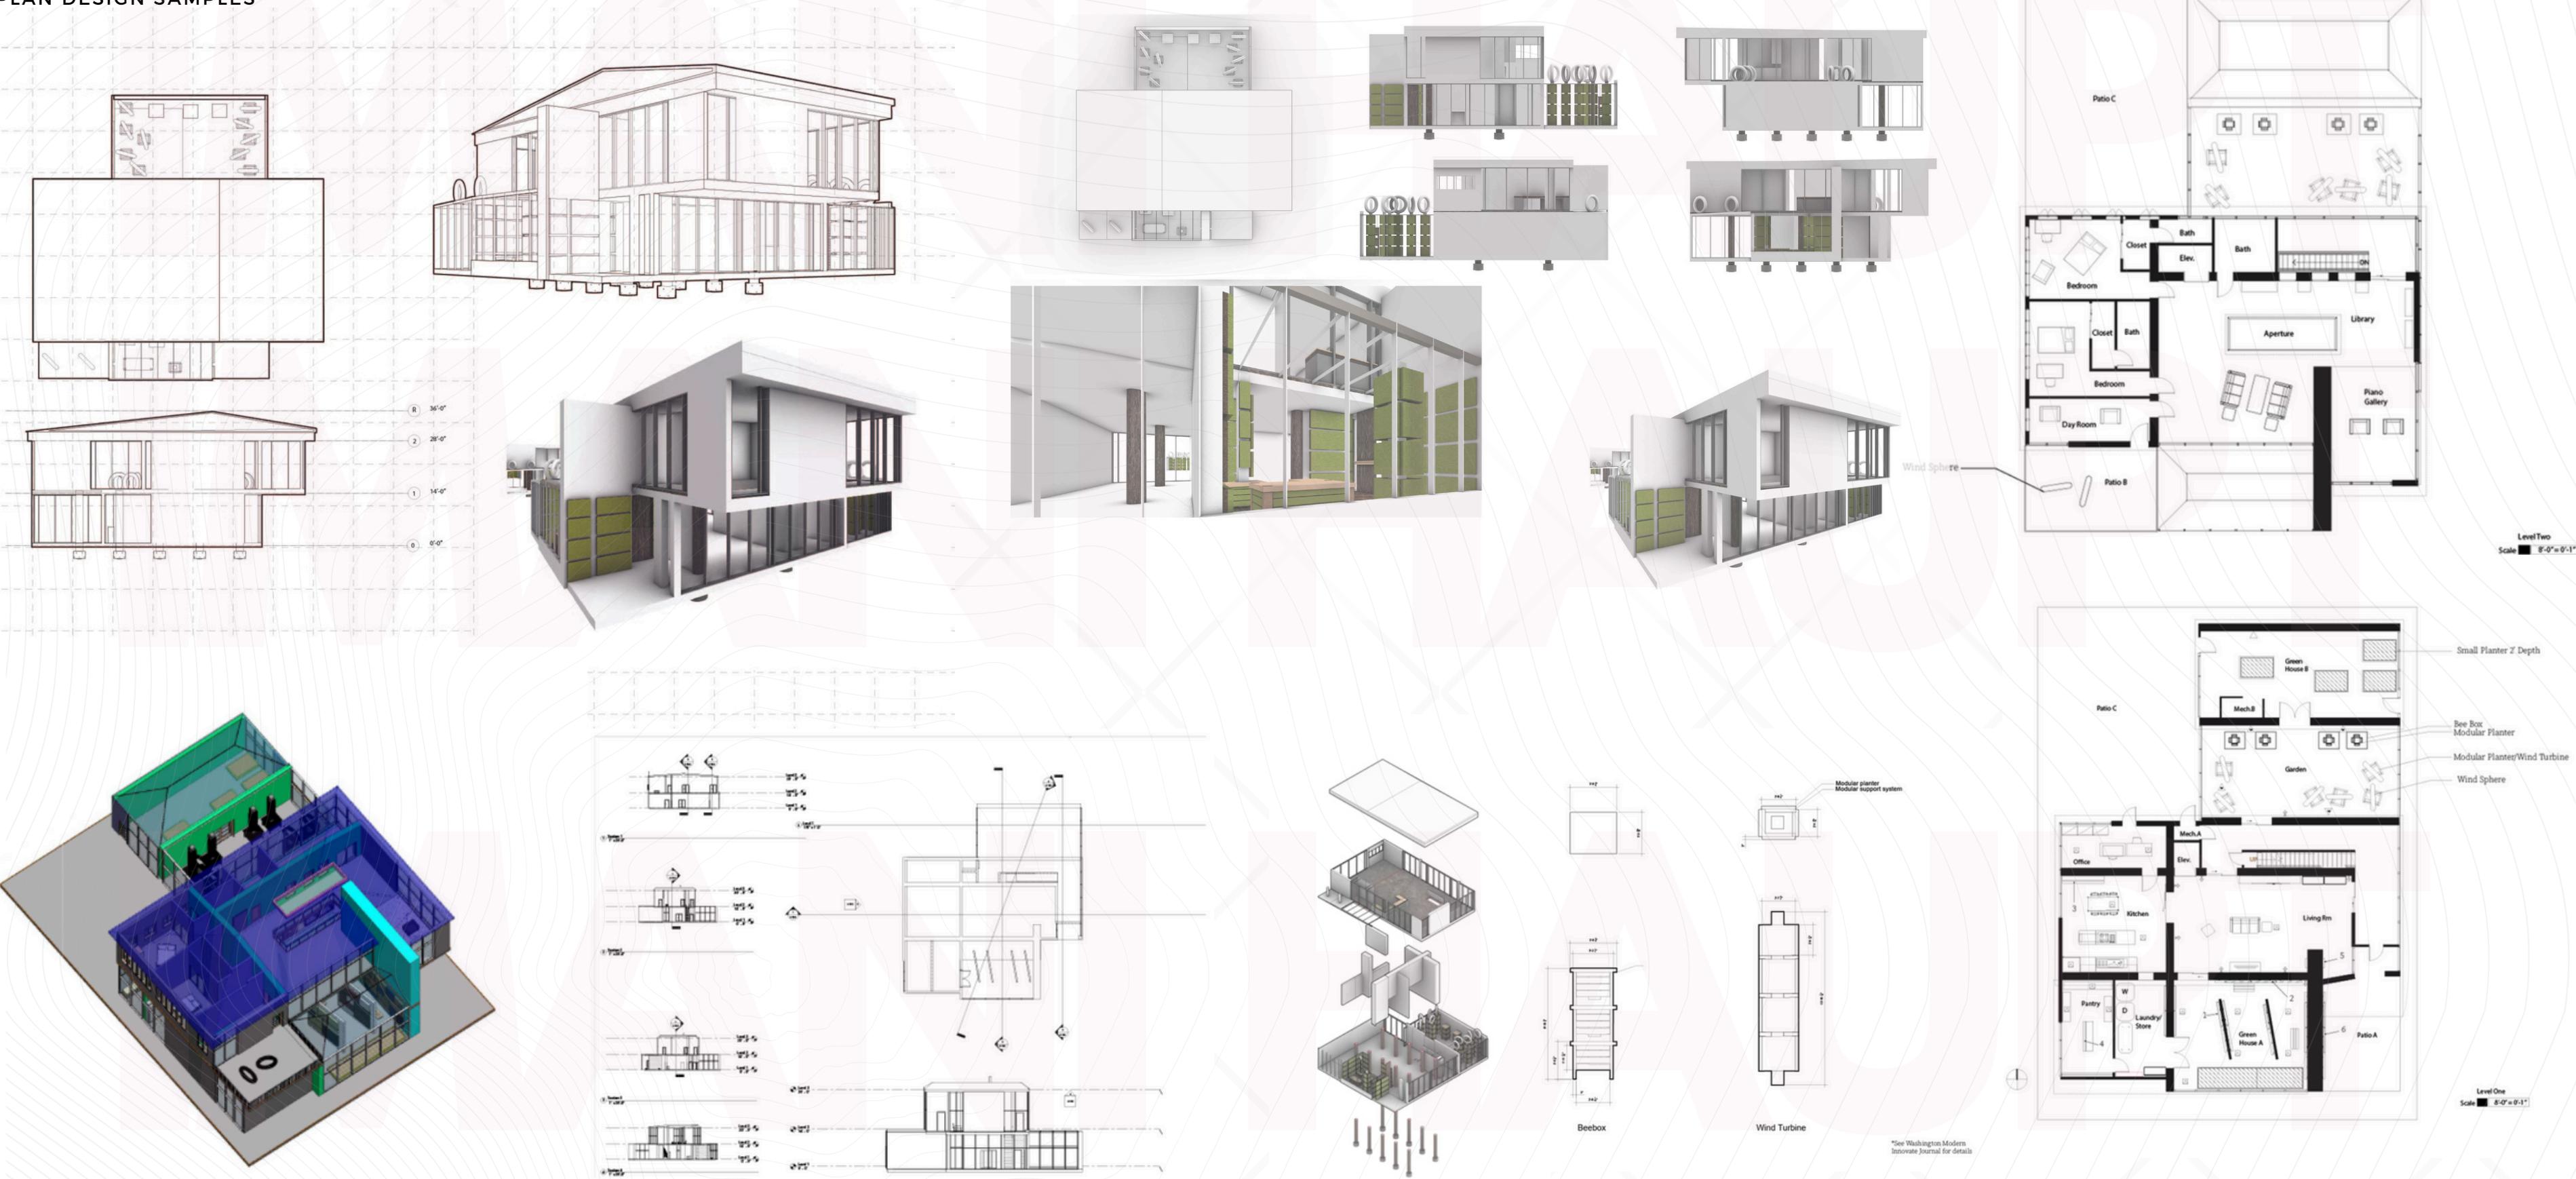

# ARCH-DESIGNER

## PLAN DESIGN SAMPLES

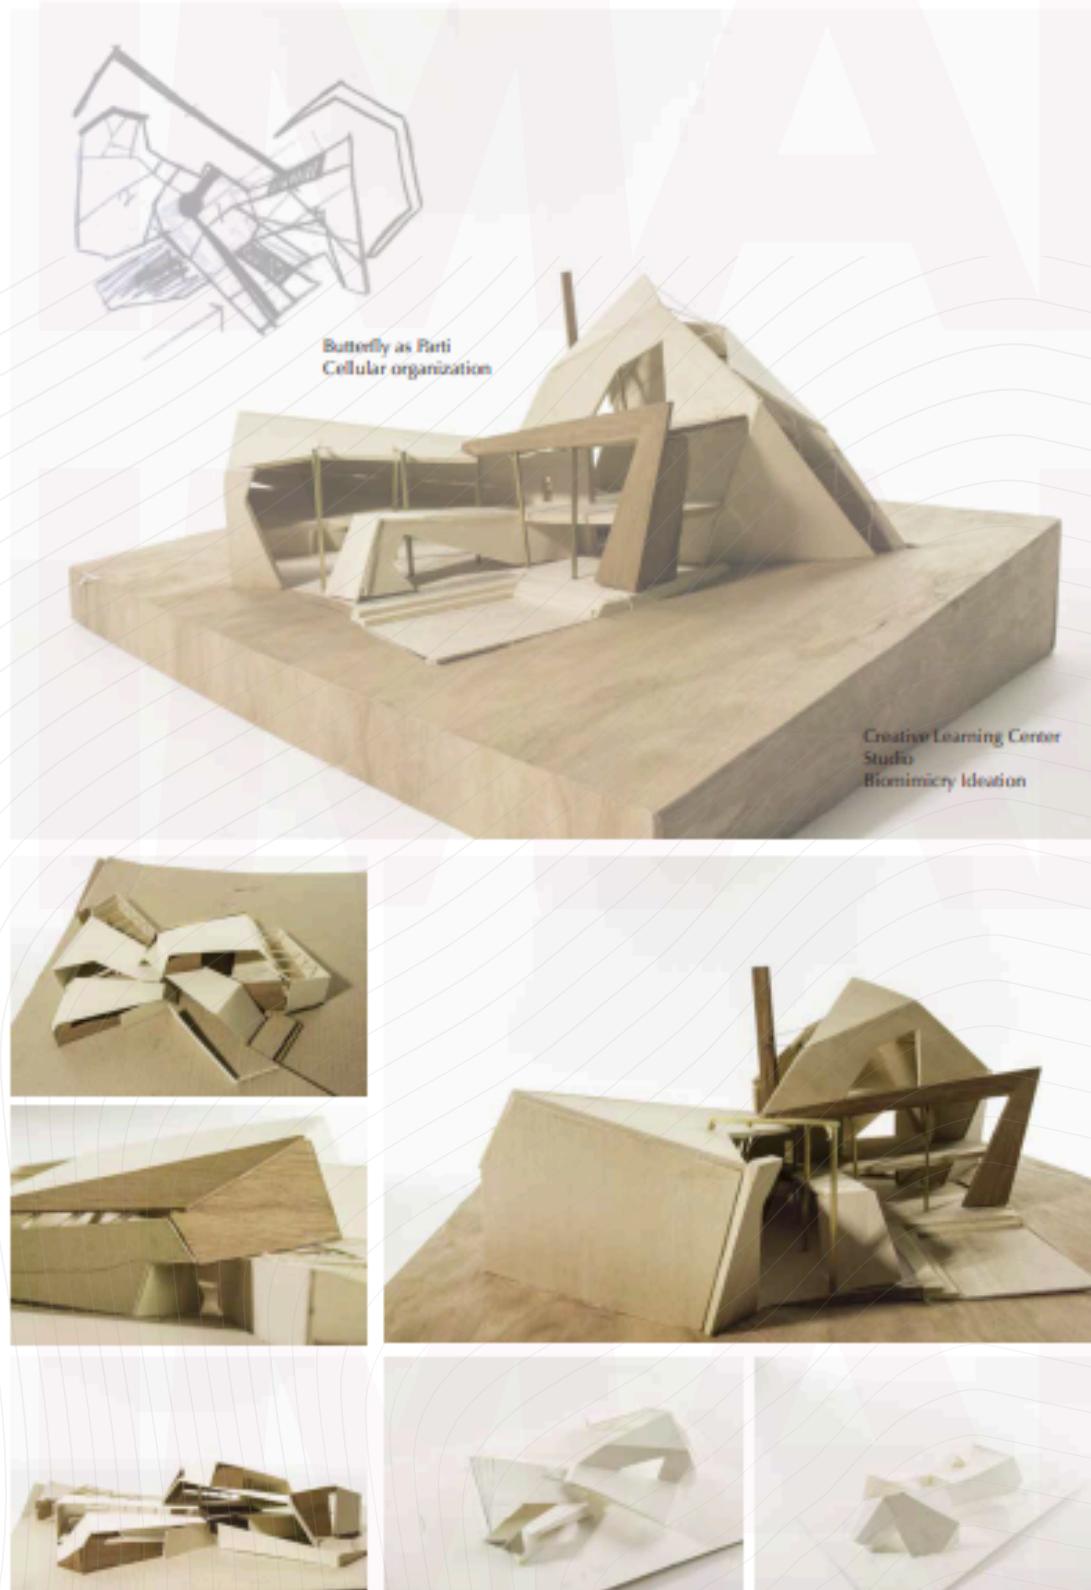


**Butterfly Mimicry:** The Design borrows its aesthetic and Parti from the butterfly. Its representative of wisdom. The cellular design and structure of the wings influences the form.



The Purpose of this design was to produce a structure that would create shade in a prairie terrain. This design does so by offering a grow wall as its skin. The walls are paneled and rotate for management. Plants can be grown along the wall and the vegetative overhang will cool inside while shading the outdoors.

A Copper Grow Wall  
Partitions rotated for maintenance  
In case of limited growth space  
Edible walls exploration

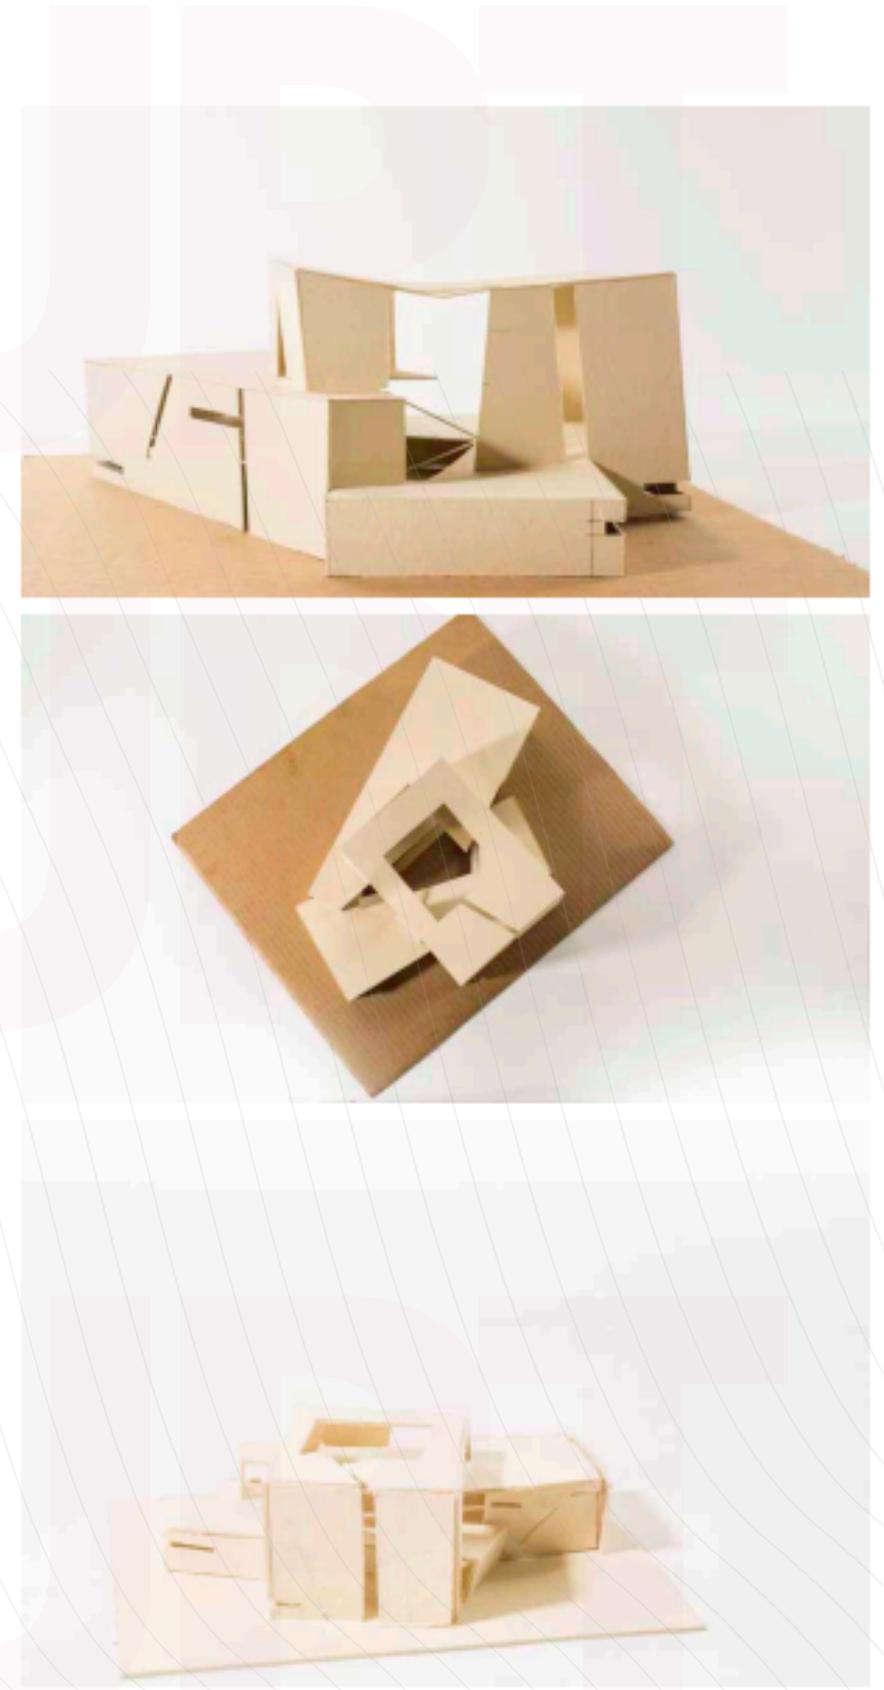

**Youth Hostel**  
Rock mimicry



To see more reach out to me on  
[linkedin.com/in/imanihaupt](https://www.linkedin.com/in/imanihaupt)

[instagram@arq.well](mailto:instagram@arq.well)

[imanihaupt.com](http://imanihaupt.com)

**IMANI HAUPT**

Email to view Architecture portfolio  
[Contact to view Web/Media design portfolio](#)